

PROJETO

CASA RICARDO

CLIENTE

Ricardo José Alves Nunes

LOCALIZAÇÃO

Rua Bernardo Marques, nº6 - Bloco C1, 1B
Santo António dos Cavaleiros - Loures

FASE

PROJETO

TIPO DE DESENHO

PLANTA DE FORROS | TETOS

CÓDIGO DO PROJETO PROJ2026_285

ESCALA

1/100

FORMATO

A3

DATA

02 / 08 / 2026

VERSÃO

06

STATUS DO DOCUMENTO

PRELIMINAR

TECNICO/A RESPONSÁVEL

Rute Frias
OA N.º 16398

DESENHADO POR

Amanda Pioner
Arquiteta

APROVADO POR

Robson Senna
COO

HISTÓRICO DE REVISÕES

REV.	DATA	DESCRIÇÃO
01	09/07/2026	Proposta de layout V1
02	10/07/2026	Alteração de layout após reunião V2
03	13/08/2026	Apresentação da decoração V1
04	21/08/2026	Alteração decoração após reunião
05	24/08/2026	Alteração decoração V2
06	02/08/2026	Apresentação de renders finais

Nº DE FOLHA


ARQ - 03

TOTAL DE FOLHAS

07

Este desenho é propriedade da Senna Building e não poderá ser reproduzido, divulgado ou copiado, total ou parcialmente, sem autorização prévia e expressa por escrito.

Todas as dimensões, cotas e condições existentes indicadas neste desenho deverão ser verificadas e confirmadas em obra antes da execução dos trabalhos.

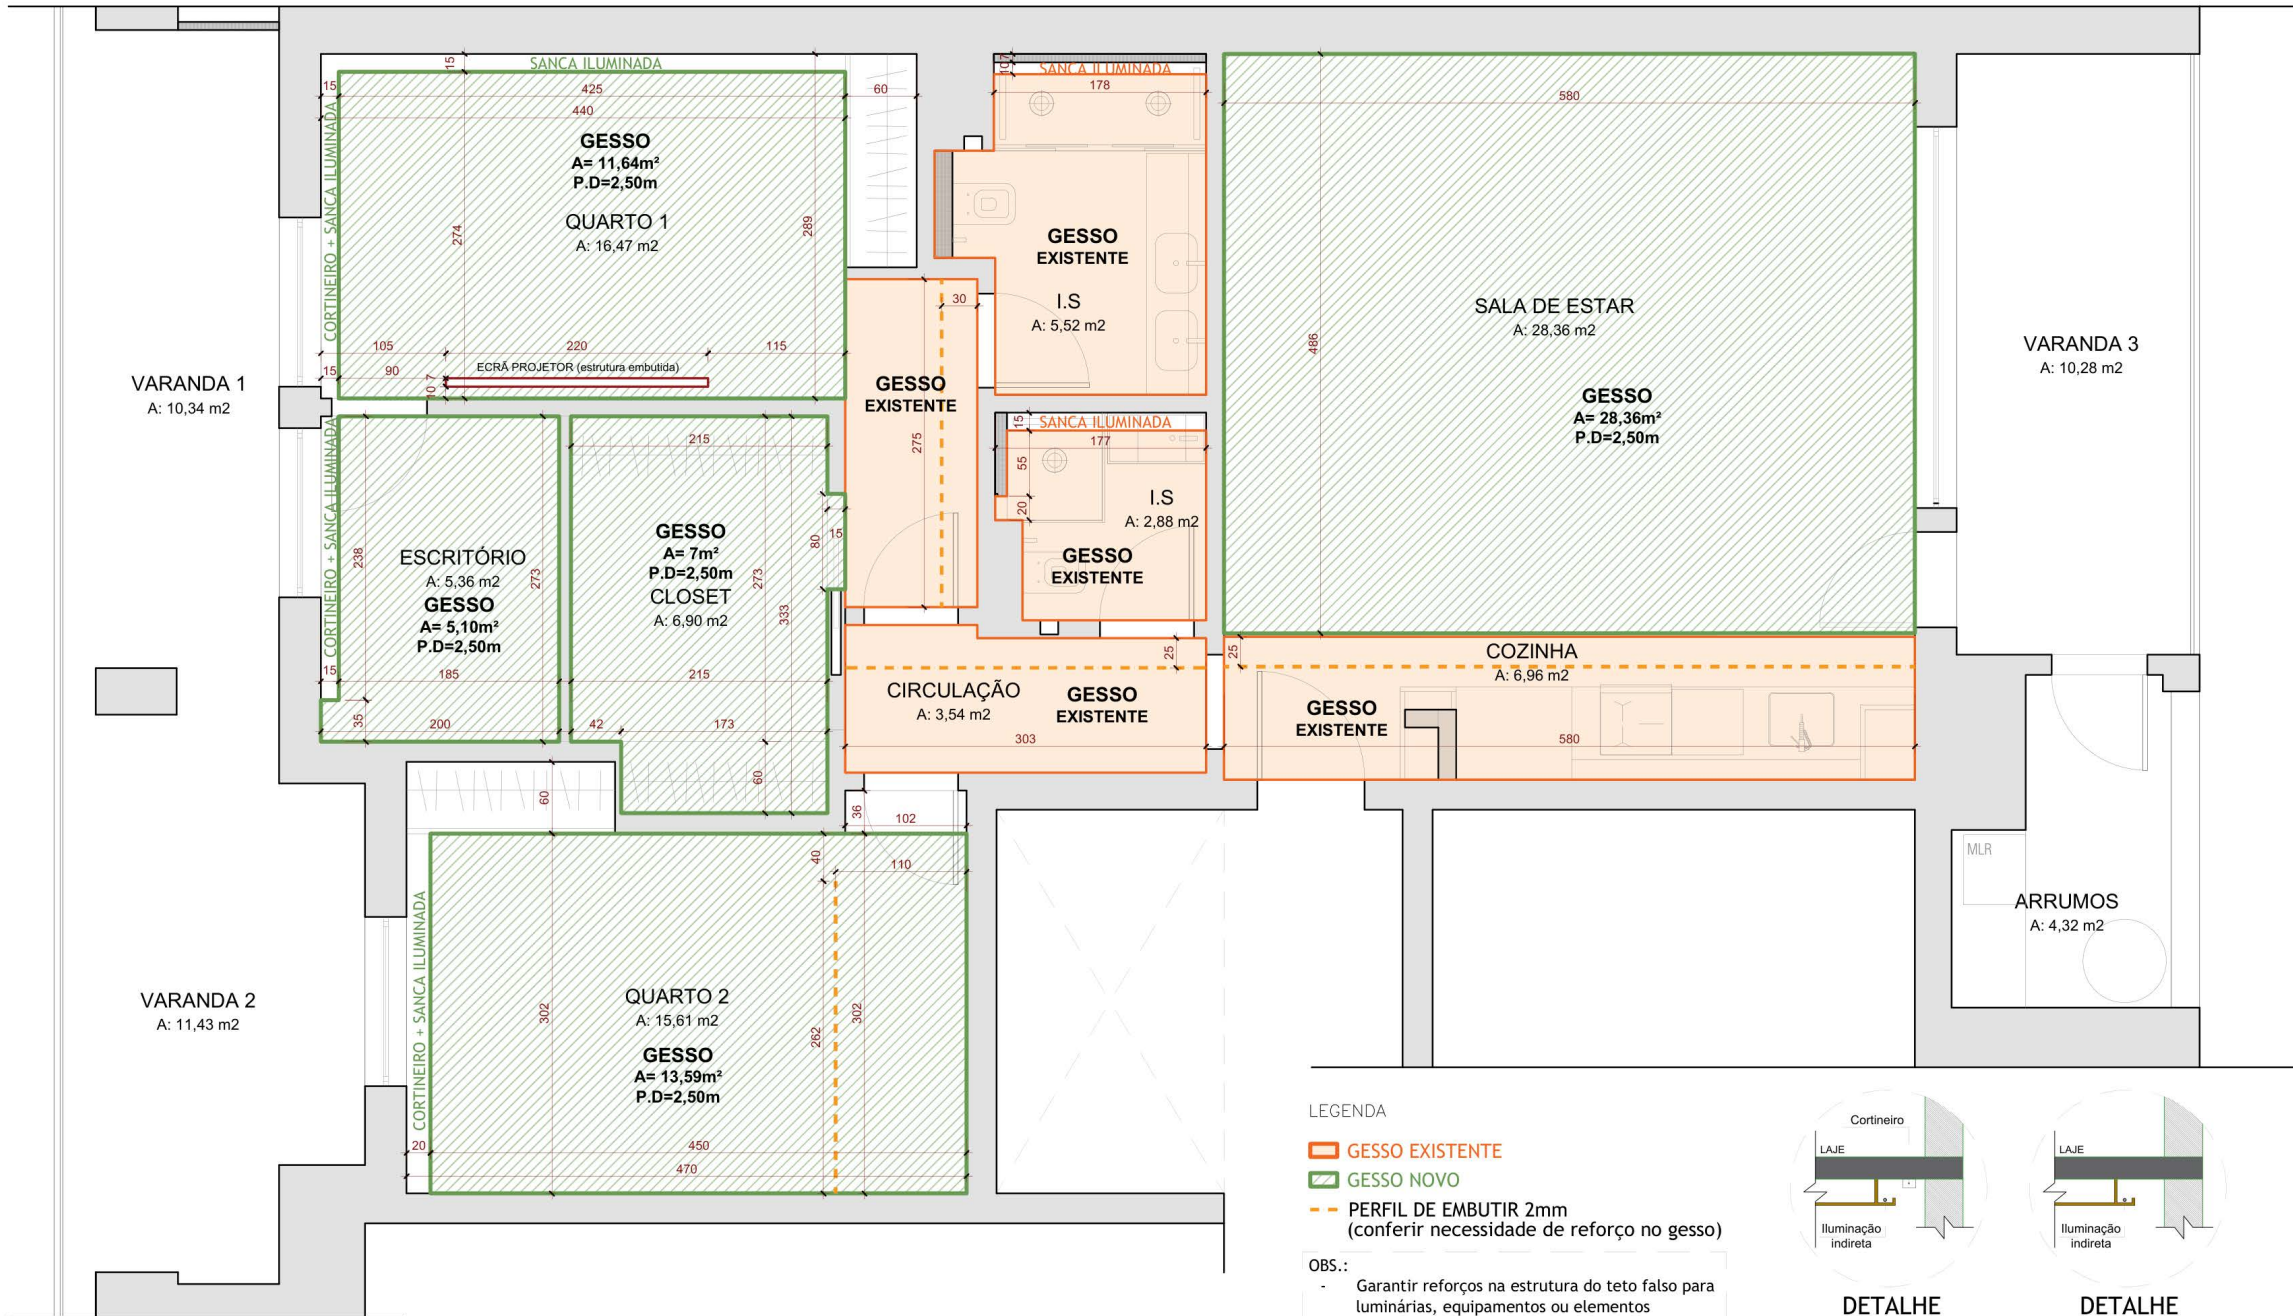


LEGENDA


- GESSO EXISTENTE
- GESSO NOVO
- PERFIL DE EMBUTIR 2mm (conferir necessidade de reforço no gesso)

OBS.:

- Garantir reforços na estrutura do teto falso para luminárias, equipamentos ou elementos suspensos que assim o exijam;
- Confirmar em obra a posição dos equipamentos embutidos antes do fecho das placas;
- Em zonas húmidas, utilizar placas e sistemas adequados às condições de humidade.

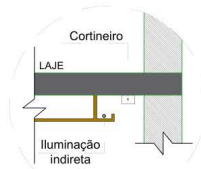

DETALHE
CORTINEIRO +
SANCA ILUMINADA

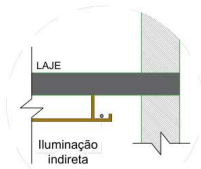

DETALHE
SANCA ILUMINADA