



+351 935 483 648



contacto@sennabuilding.com

PROJETO

CASA RICARDO

CLIENTE

Ricardo José Alves Nunes

LOCALIZAÇÃO

Rua Bernardo Marques, nº6 - Bloco C1, 1B
Santo António dos Cavaleiros - Loures

FASE

PROJETO

TIPO DE DESENHO

PLANTA DE NECESSIDADES DE HIDRAULICA

CÓDIGO DO PROJETO

PROJ2026_285

ESCALA

1/100

FORMATO

A3

DATA

02 / 08 / 2026

VERSÃO

06

STATUS DO DOCUMENTO

PRELIMINAR

TECNICO/A RESPONSÁVEL

Rute Frias
OA N.º 16398

DESENHADO POR

Amanda Pioner
Arquiteta

APROVADO POR

Robson Senna
COO

HISTÓRICO DE REVISÕES

REV.	DATA	DESCRIÇÃO
01	09/07/2026	Proposta de layout V1
02	10/07/2026	Alteração de layout após reunião V2
03	13/08/2026	Apresentação da decoração V1
04	21/08/2026	Alteração decoração após reunião
05	24/08/2026	Alteração decoração V2
06	02/08/2026	Apresentação de renders finais

Nº DE FOLHA


ARQ - 04

TOTAL DE FOLHAS

07

Este desenho é propriedade da Senna Building e não poderá ser reproduzido, divulgado ou copiado, total ou parcialmente, sem autorização prévia e expressa por escrito.

Todas as dimensões, cotas e condições existentes indicadas neste desenho deverão ser verificadas e confirmadas em obra antes da execução dos trabalhos.

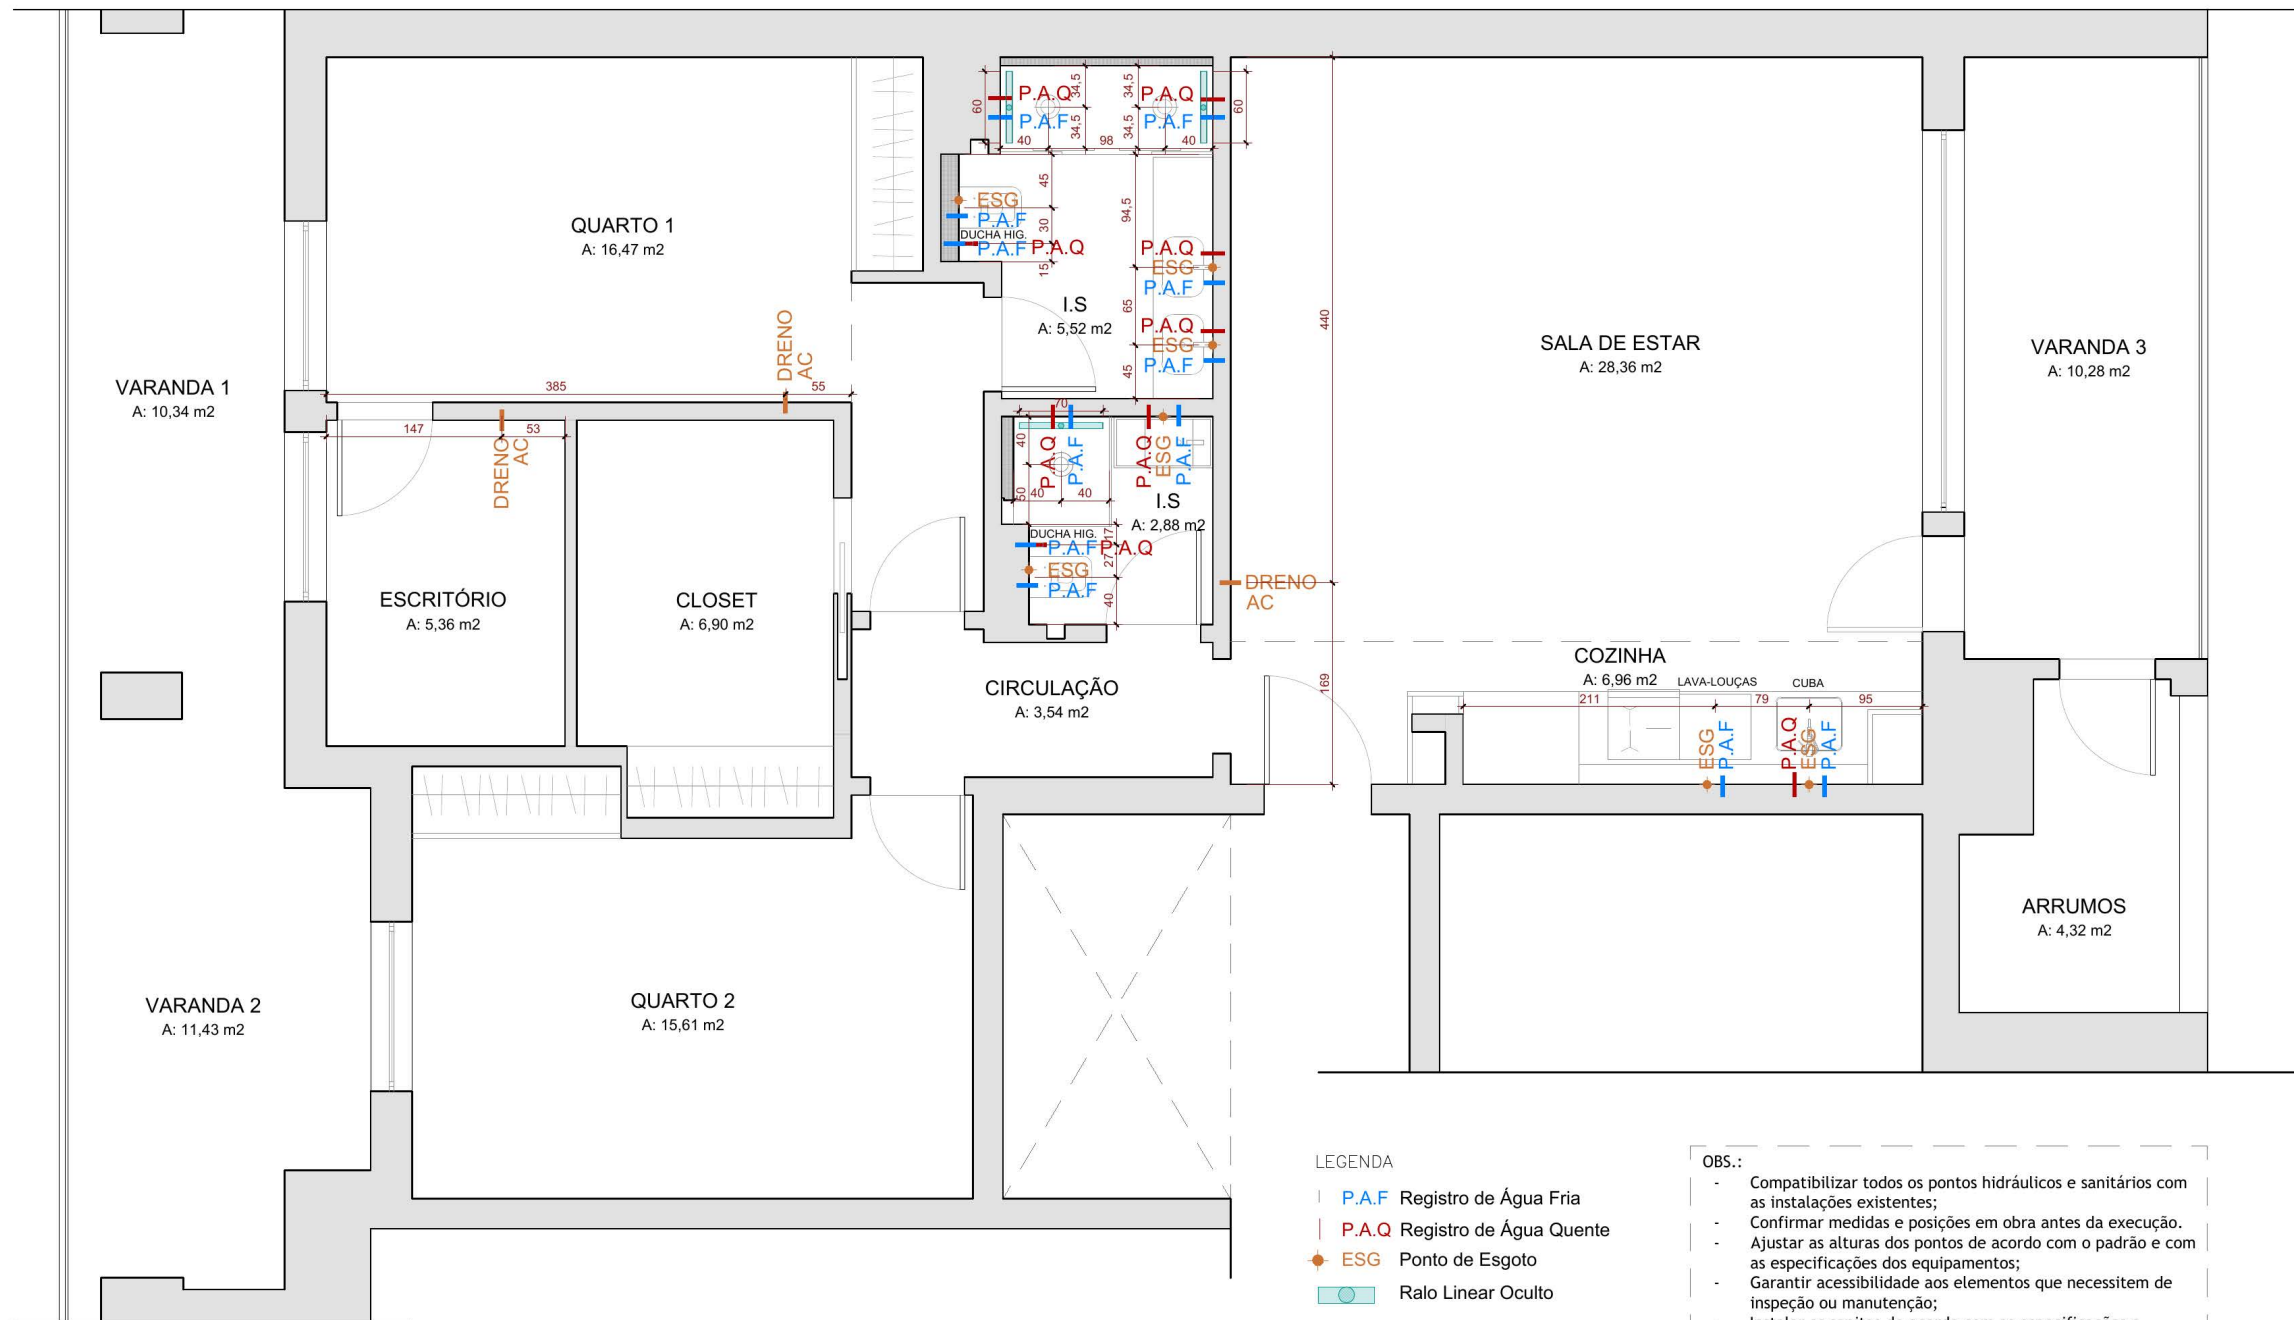

LEGENDA

- P.A.F Registro de Água Fria
- P.A.Q Registro de Água Quente
- ESG Ponto de Esgoto
- Ralo Linear Oculto

OBS.:

- Compatibilizar todos os pontos hidráulicos e sanitários com as instalações existentes;
- Confirmar medidas e posições em obra antes da execução.
- Ajustar as alturas dos pontos de acordo com o padrão e com as especificações dos equipamentos;
- Garantir acessibilidade aos elementos que necessitem de inspeção ou manutenção;
- Instalar as sanitas de acordo com as especificações e instruções do fabricante.