

PROJETO

CASA RICARDO

CLIENTE

Ricardo José Alves Nunes

LOCALIZAÇÃO

Rua Bernardo Marques, nº6 - Bloco C1, 1B
Santo António dos Cavaleiros - Loures

FASE

PROJETO

TIPO DE DESENHO

PLANTA DE NECESSIDADES ELÉTRICAS

CÓDIGO DO PROJETO PROJ2026_285

ESCALA

1/100

FORMATO

A3

DATA

02 / 08 / 2026

VERSÃO

06

STATUS DO DOCUMENTO

PRELIMINAR

TECNICO/A RESPONSÁVEL

Rute Frias
OA N.º 16398

DESENHADO POR

Amanda Pioner
Arquiteta

APROVADO POR

Robson Senna
COO

HISTÓRICO DE REVISÕES

REV.	DATA	DESCRIÇÃO
01	09/07/2026	Proposta de layout V1
02	10/07/2026	Alteração de layout após reunião V2
03	13/08/2026	Apresentação da decoração V1
04	21/08/2026	Alteração decoração após reunião
05	24/08/2026	Alteração decoração V2
06	02/08/2026	Apresentação de renders finais

Nº DE FOLHA


ARQ - 06

TOTAL DE FOLHAS

07

Este desenho é propriedade da Senna Building e não poderá ser reproduzido, divulgado ou copiado, total ou parcialmente, sem autorização prévia e expressa por escrito.

Todas as dimensões, cotas e condições existentes indicadas neste desenho deverão ser verificadas e confirmadas em obra antes da execução dos trabalhos.

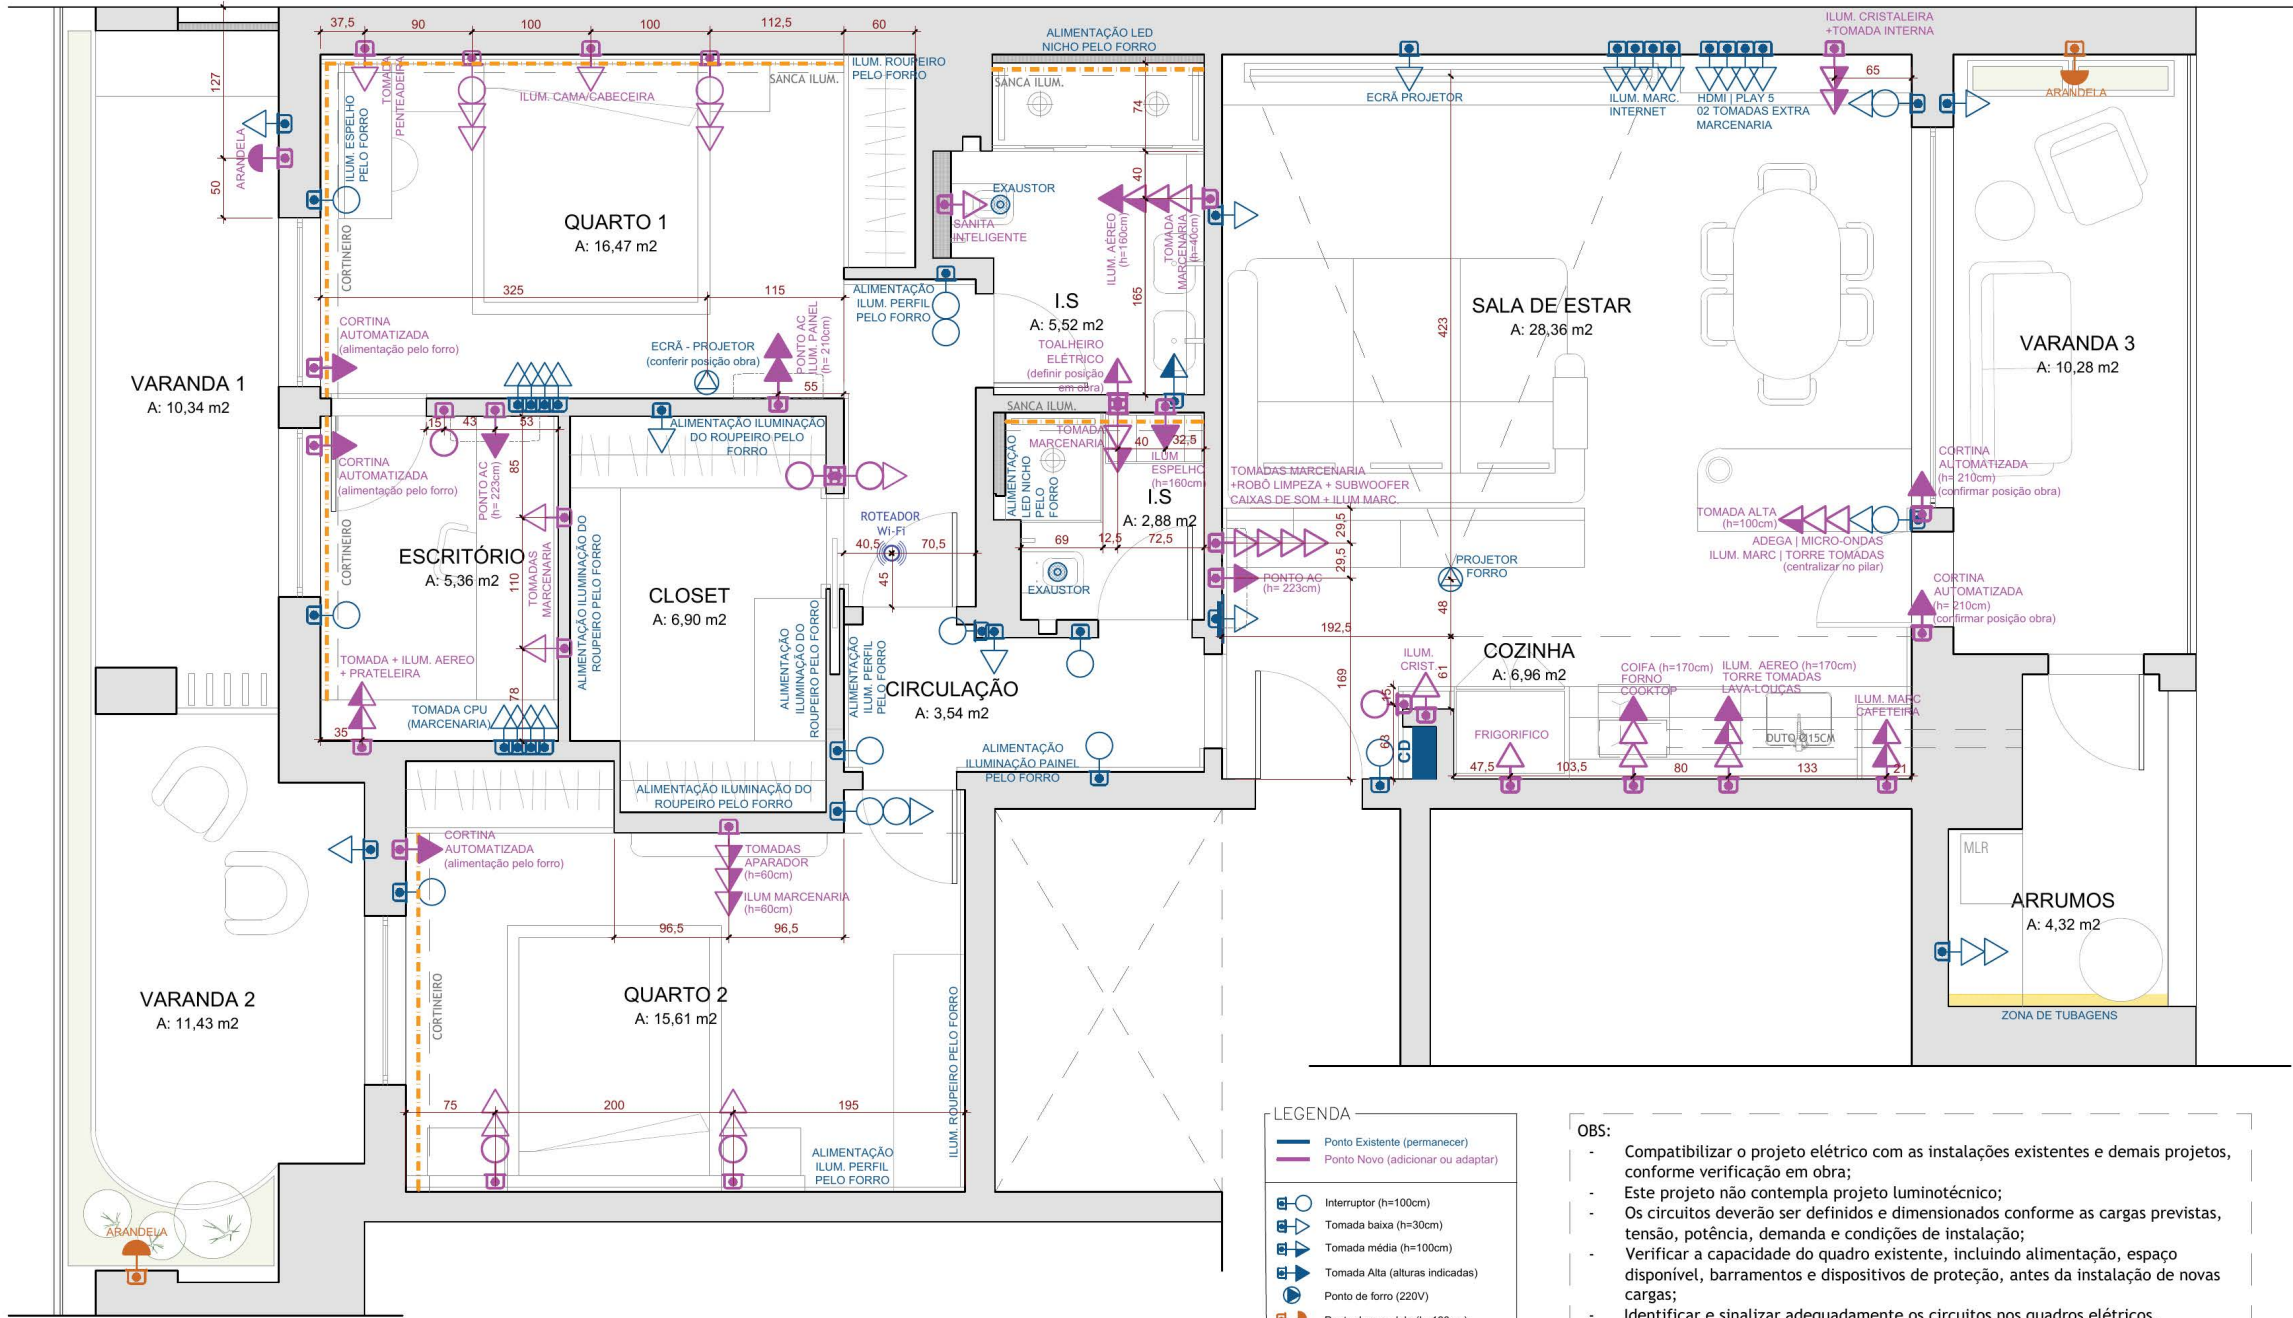

- LEGENDA
- Ponto Existente (permanecer)
 - Ponto Novo (adicionar ou adaptar)
 - Interruptor (h=100cm)
 - Tomada baixa (h=30cm)
 - Tomada média (h=100cm)
 - Tomada Alta (alturas indicadas)
 - Ponto de forno (220V)
 - Ponto de arandela (h=160cm)
 - Sanca iluminada

- OBS:
- Compatibilizar o projeto elétrico com as instalações existentes e demais projetos, conforme verificação em obra;
 - Este projeto não contempla projeto luminotécnico;
 - Os circuitos deverão ser definidos e dimensionados conforme as cargas previstas, tensão, potência, demanda e condições de instalação;
 - Verificar a capacidade do quadro existente, incluindo alimentação, espaço disponível, barramentos e dispositivos de proteção, antes da instalação de novas cargas;
 - Identificar e sinalizar adequadamente os circuitos nos quadros elétricos, mantendo a organização, identificação e acessibilidade dos dispositivos;
 - Antes da execução, todas as medidas, posições e condições existentes deverão ser conferidas em obra. Eventuais divergências entre o projeto e a situação encontrada deverão ser comunicadas ao responsável técnico.